# Plan v29 — Piscine multi-zones Lennon

v29 : corrections finales — gap sol lounge comblé, textes Plage A centrés, labels escalier repositionnés, Jardin remonté

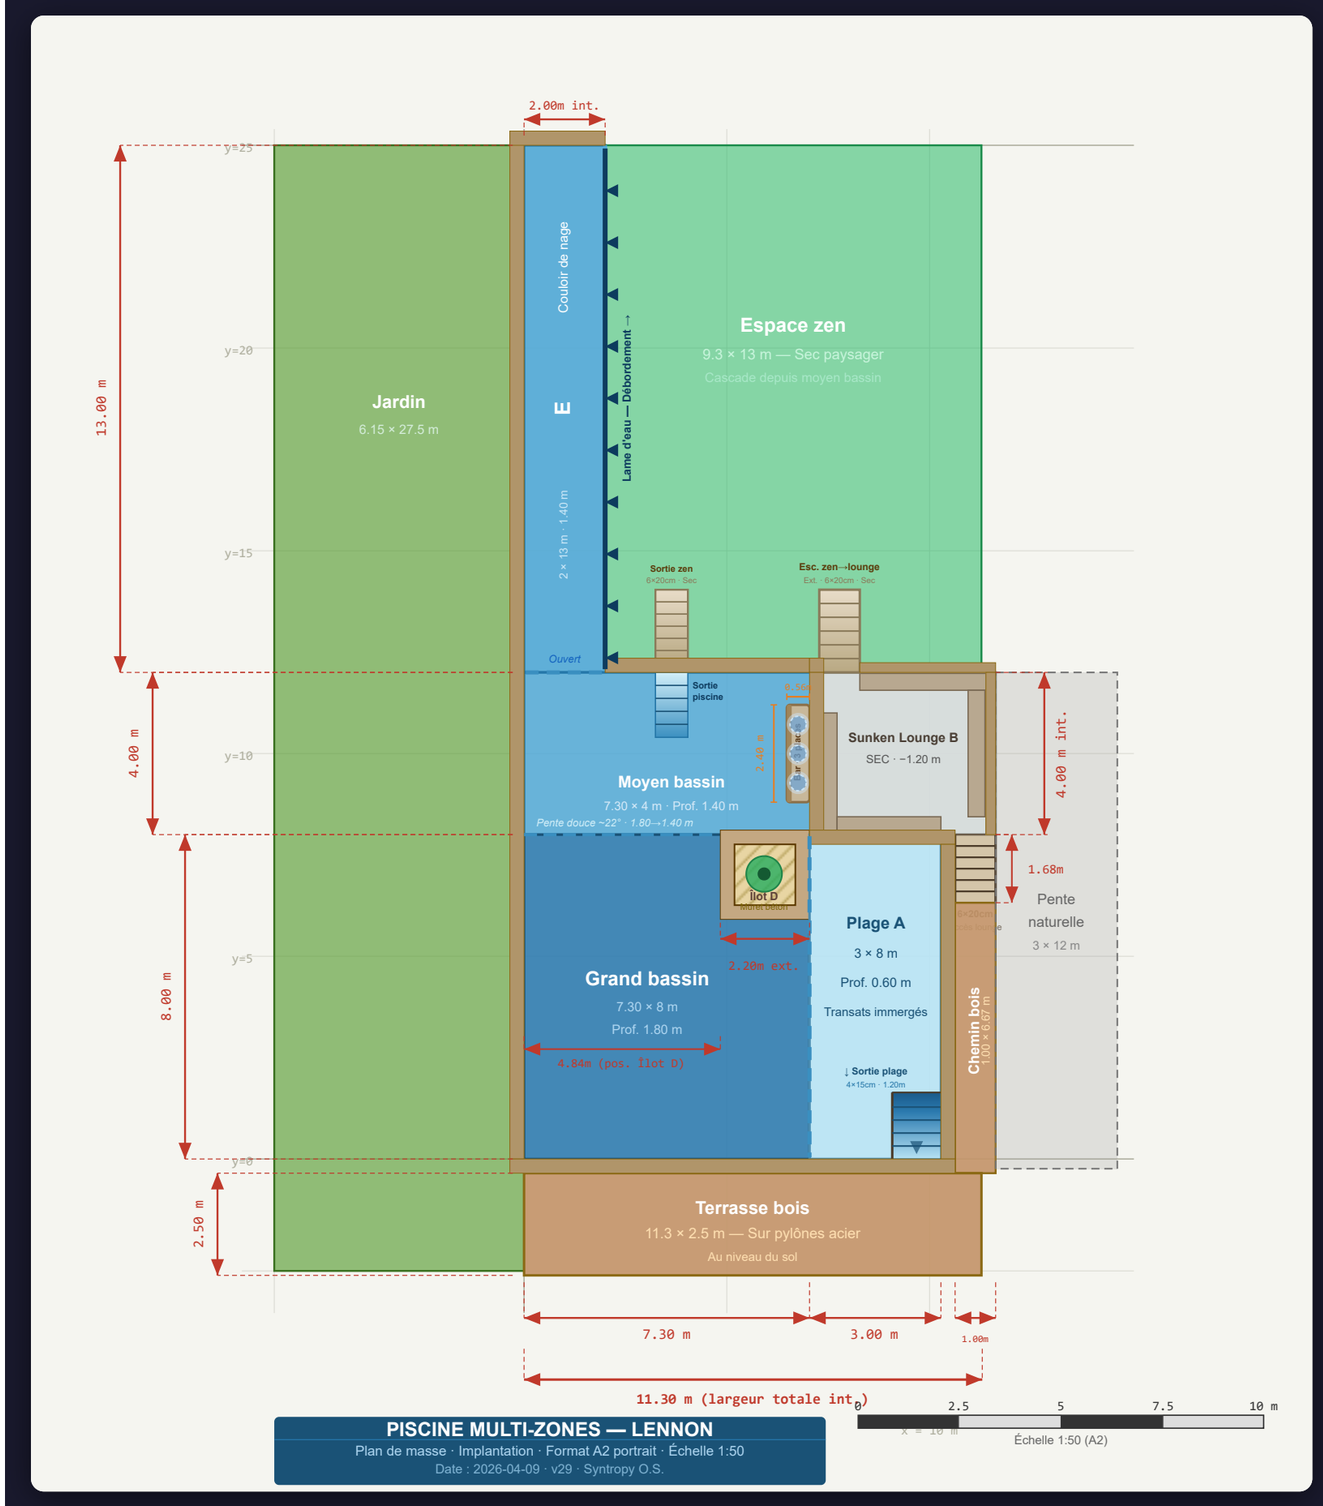


## LÉGENDE

- Grand bassin 1.80 m
- Moyen bassin / Couloir 1.40 m
- Plage californienne 0.60 m
- Sunken Lounge SEC −1.20m
- Banquettes (4 côtés)
- Extension bar (tablette 0.56m)
- Escalier aquatique (×2)
- Escalier ext. zen→lounge
- Escalier lounge (6×20cm)
- Murs eau 35cm (agglos 30+5cm)
- Murs secs 24cm (lounge N+E)
- Terrasse / Chemin bois
- Îlot D — Muret béton
- Tabourets ×3 Ø38cm (glissés sous tablette)
- Jardin
- Espace zen

## CIRCULATIONS V11

**↑ Moyen bassin → Zen [NOUVEAU]**
10 marches · h=14.5cm · g=31cm
Larg. 1.20m · NF P90-308 ✓

**↑ Piscine → Espace zen**
9 marches · giron 30cm
Larg. 80cm · NF P90-308 ✓

**↓ Espace zen → Lounge [NOUVEAU]**
6 marches ext. · 20cm chacune
Larg. 1.00m · Sec · NF P01-012 ✓

**↓ Terrasse → Lounge**
6 marches · 20cm chacune
Larg. 1.00m · Emprise 1.68m

## MURS BÉTON — OUVERTURES

■ Mur nord (3 segments) :
x=295.25→354 (couloir)
x=354→480 (segment A — étendu v16)
x=511→592 (segment B)
○ Ouverture x=354→384 : esc. zen
○ Ouverture x=480→511 : esc. ext. zen→lounge

## EXTENSION BAR V16

Tablette : **0.56 × 2.40m**
Tabourets : **×3 · Ø38cm**
Espacement : **70cm axe-à-axe**
Dégagement genoux : **55cm libre**

## DIMENSIONS INTERNES

Couloir : **2.00m × 13.00m**
Moyen bassin : **7.30 × 4.00m**
Grand bassin : **7.30 × 8.00m**
Lounge : **4.00 × 4.00m**
Plage : **3.00 × 8.00m**
Lounge libre : **~3.00 × 3.12m**

## SURFACES EAU

Grand bassin : 53.6 m²
Moyen bassin : 29.2 m²
Couloir : 26.0 m²
Plage : 24.0 m²
**Eau ≈ 132.8 m²**